


PROPOSED LAYOUT PLAN OF PHASE 'B&K' DREAM CITY - II (Part) IN SY.NO'S 264, 266 TO 272, 274, 275, 276, 277, & 278, SITUATED AT KHALSA IBRAHIMPATAN VILLAGE & MANDAL, RANGA REDDY DIST,

Belongs to :-


**Sri T.V. RAMANA MURTHY. S/o Sri. T. RAMAKRISHNA MURTY.
AND OTHER'S.**

AREAS:-

PLOTTED AREA : 5,90,072.00 Sq.Yds OR 121 Ac. 36.60 Gts.
ROADS & PUBLIC AREA : 3,56,995.00 Sq.Yds OR 73 Ac. 30.40 Gts.
TOTAL LAND AREA : 9,47,067.00 Sq.Yds OR 195 Ac. 27.00 Gts.

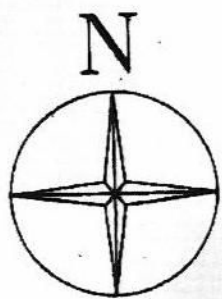


Scale : 1" = 200'

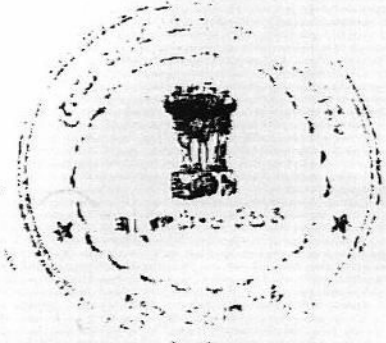

Layout plan is here by Approved
Vide P.R.No 5(65) dt. 25-10-99

P. Lem
Ranga Reddy

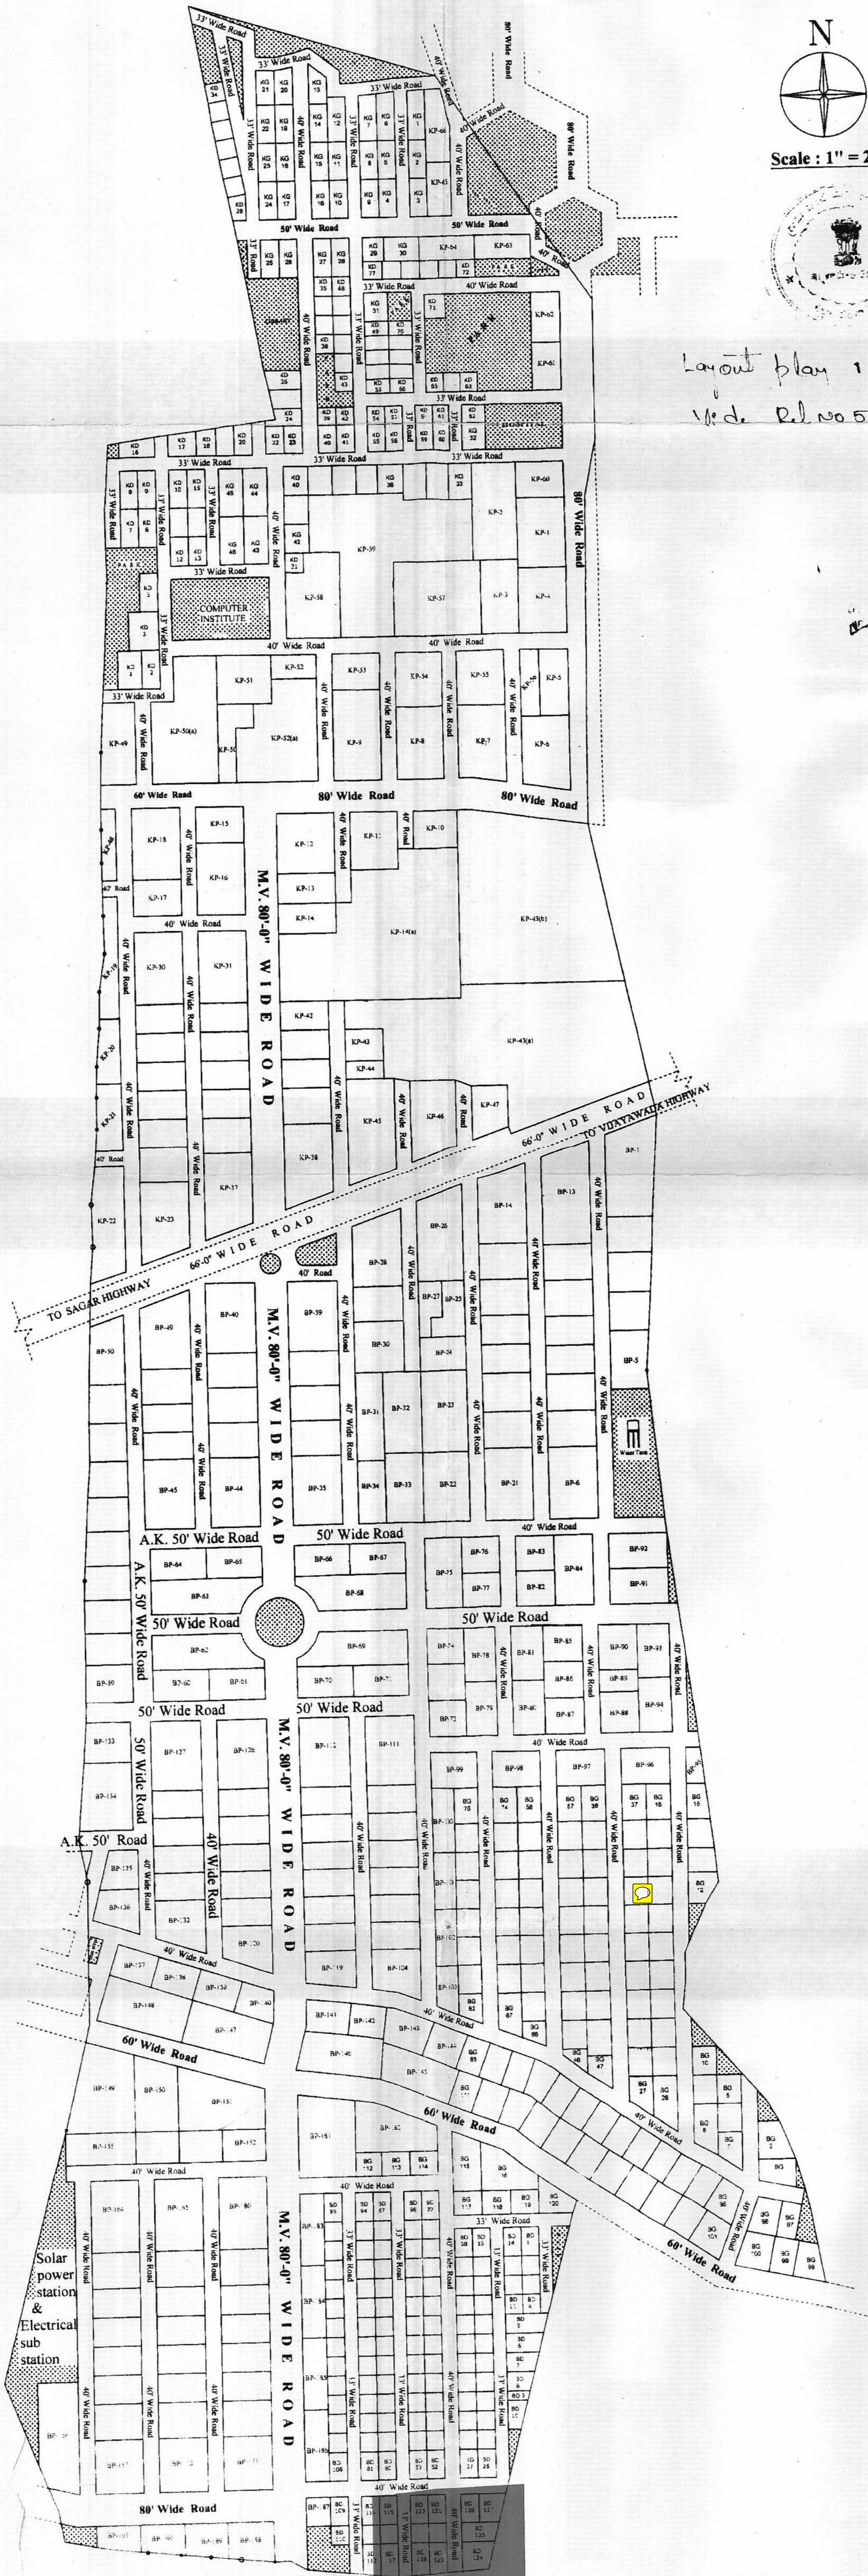


OWNER'S SIGNATURE