


**PROPOSED LAYOUT PLAN OF PHASE ' D ' DREAM CITY - II (Part)
IN SURVEY NO'S : 555 AND 556 , SITUATED AT RAIPOL Village ,
IBRAHIMPATAN Mandal , RANGA REDDY Dist.**


**Belongs to :- M/s. JANA HARSHA ESTATES 'N' CONSTRUCTIONS Pvt. Ltd.
REPRESENTED BY ITS MANAGING DIRECTOR.
Sri T.V. RAMANA MURTHY S/o Sri. T. RAMAKRISHNA MURTHY.**

AREAS:-

PLOTTED AREA	: 36756.82 Sq.Yds OR 7 Ac. 23.77 Gts.
ROADS AREA	: 19,992.83 Sq.Yds OR 4 Ac. 5.23 Gts.
TOTAL LAND AREA	: 56749.7 Sq.Yds OR 11 Ac. 29.00 Gts.

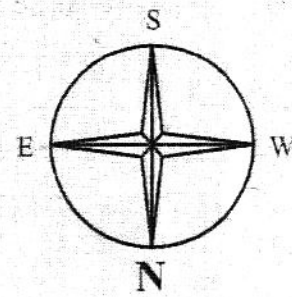

Scale : 1" = 100'

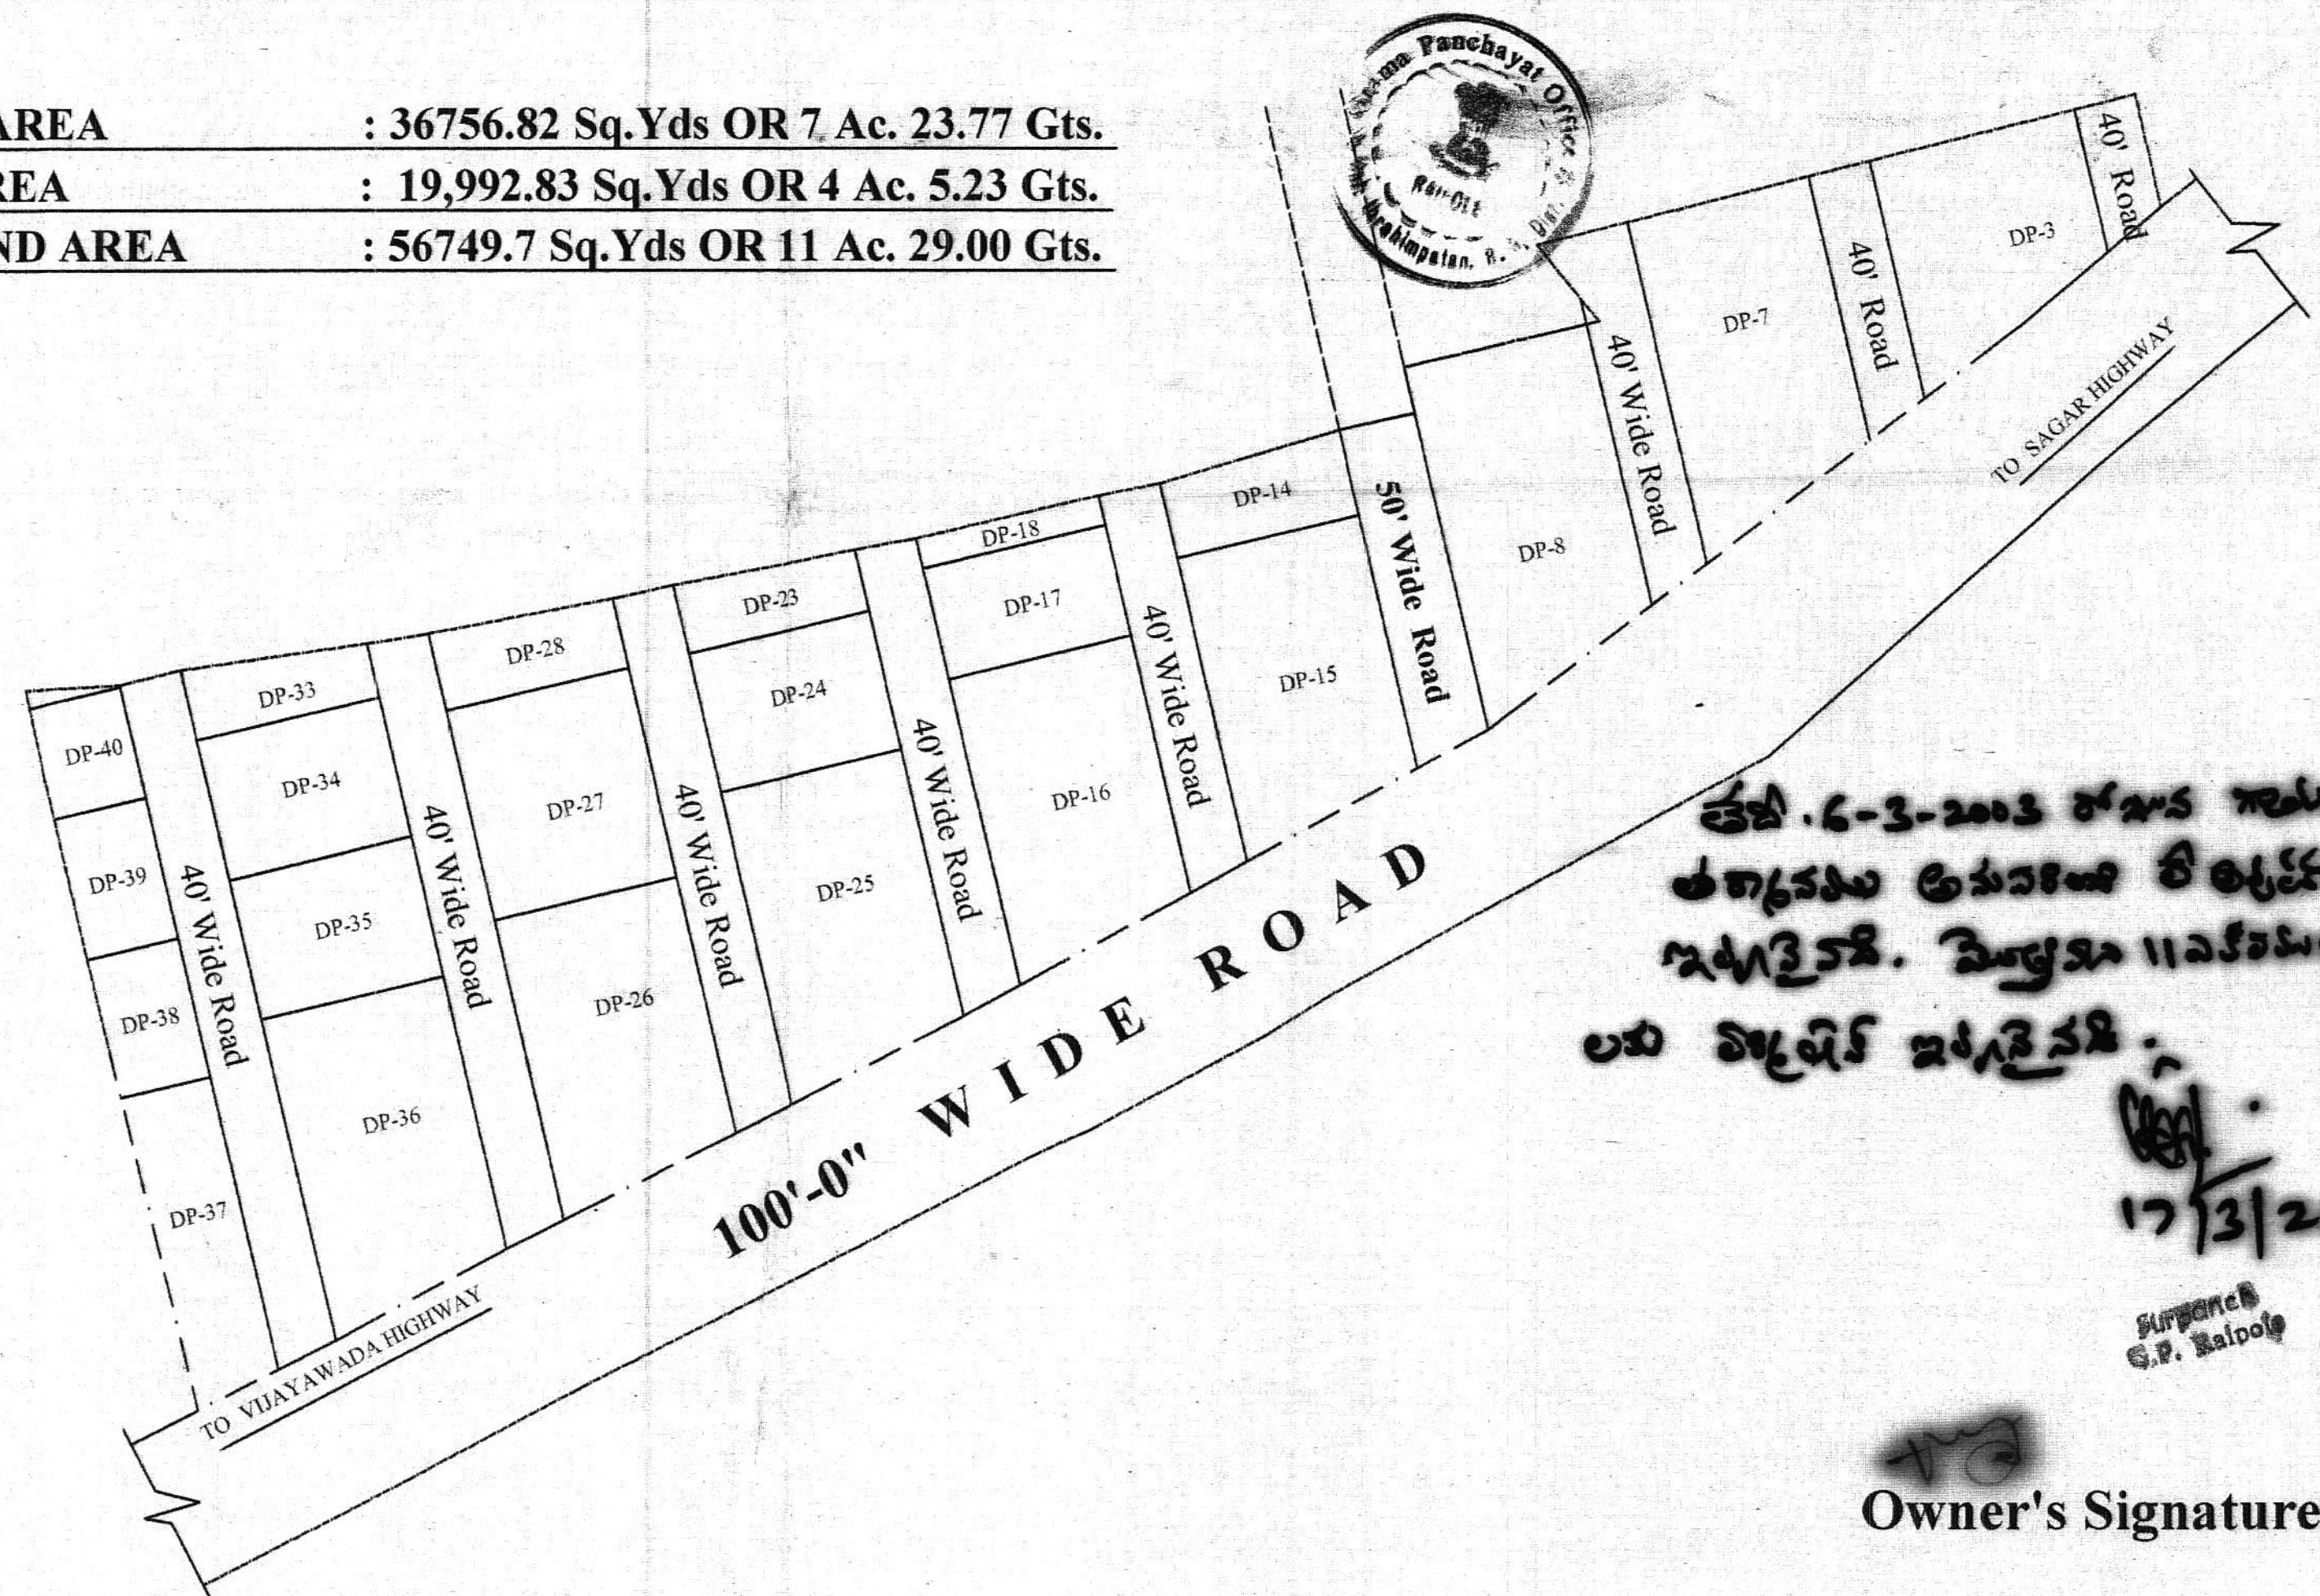

తేదీ. 6-3-2003 తన వాస్తవ స్థల వివరాలను
అధికారికి తెలియజేసి తీసుకున్న
ఇచ్చినది. పత్రం 11 ఎం.ఎం.ఎం.ఎం.
లకు విచ్చేసి ఇచ్చినది.

17/3/2003

Surgeon
G.P. Raipol

Owner's Signature