


PROPOSED LAYOUT PLAN OF PHASE ' N ' DREAM CITY - II (Part) IN SURVEY NO'S : 237, 238, 239, 240, 241, 242, 243, 244, 245, 246, 247, 248, 249, 250, 251, 252, 253, 254, 255, 256, 257, 258, 259, 260, 262, 263, 264, 265, 266, 267, 268, 271, 272 & 273 SITUATED AT NAGANPALLY Village, IBRAHIMPATAN Mandal , RANGA REDDY Dist.

BELONGS TO:-

M/s. JANAHARSHA ESTATES 'N' CONSTRUCTIONS Pvt. Ltd.
M/s. JANAHARSHA FARM LANDS Pvt. Ltd., Rep By its Director, G.P.A. HOLDER,
Sri CH. V. S. R. RAVI KUMAR S/o Sri. V. V. N. K. SOMAYAJI & OTHERS

AREAS:-

PLOTTED AREA	: 8,29,334.00 Sq.Yds OR 171 Ac. 14 Gts.
ROAD & PUBLIC AREA	: 5,55,390.00 Sq.Yds OR 114 Ac. 30 Gts.
TOTAL LAND AREA	: 13,84,724.00 Sq.Yds OR 286 Ac. 04 Gts.

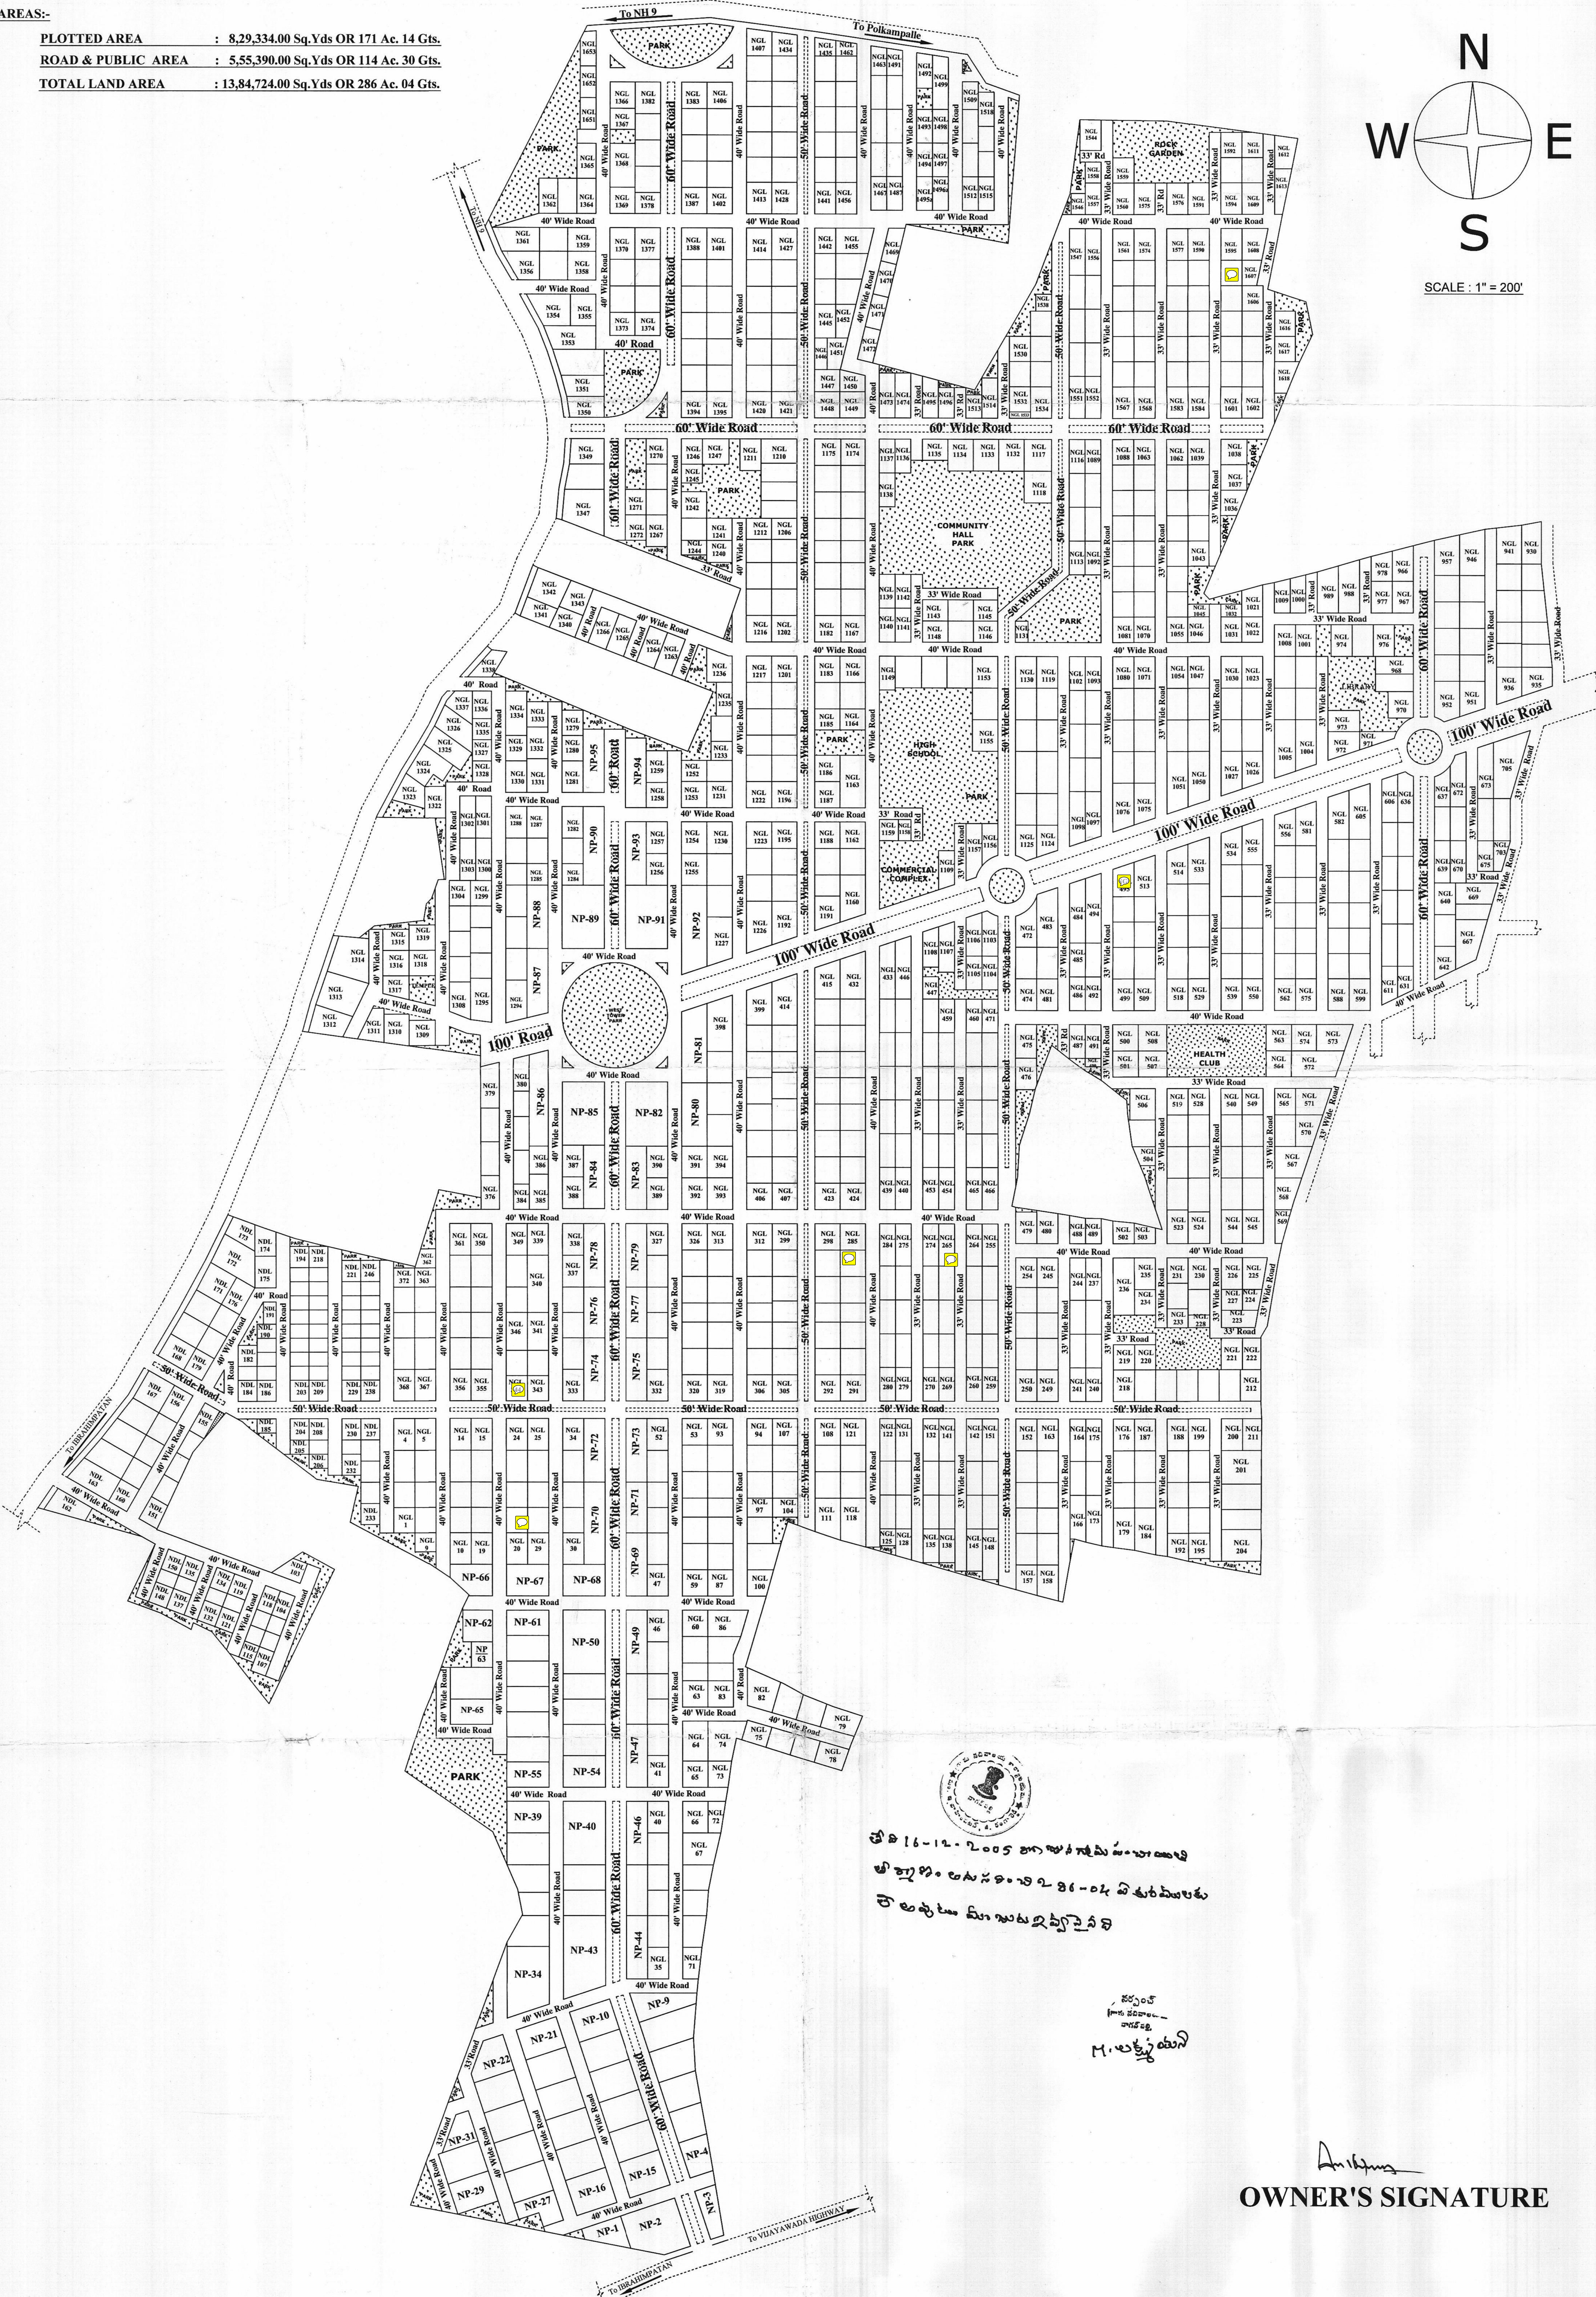

తేది 16-12-2005 నానా అసెస్మెంట్ నంబర్
ఆర్డర్ నంబర్ 281-04 విశ్రాంతి
ఆర్డర్ నంబర్ మూలము
హ.అ.కృష్ణయ్య

OWNER'S SIGNATURE